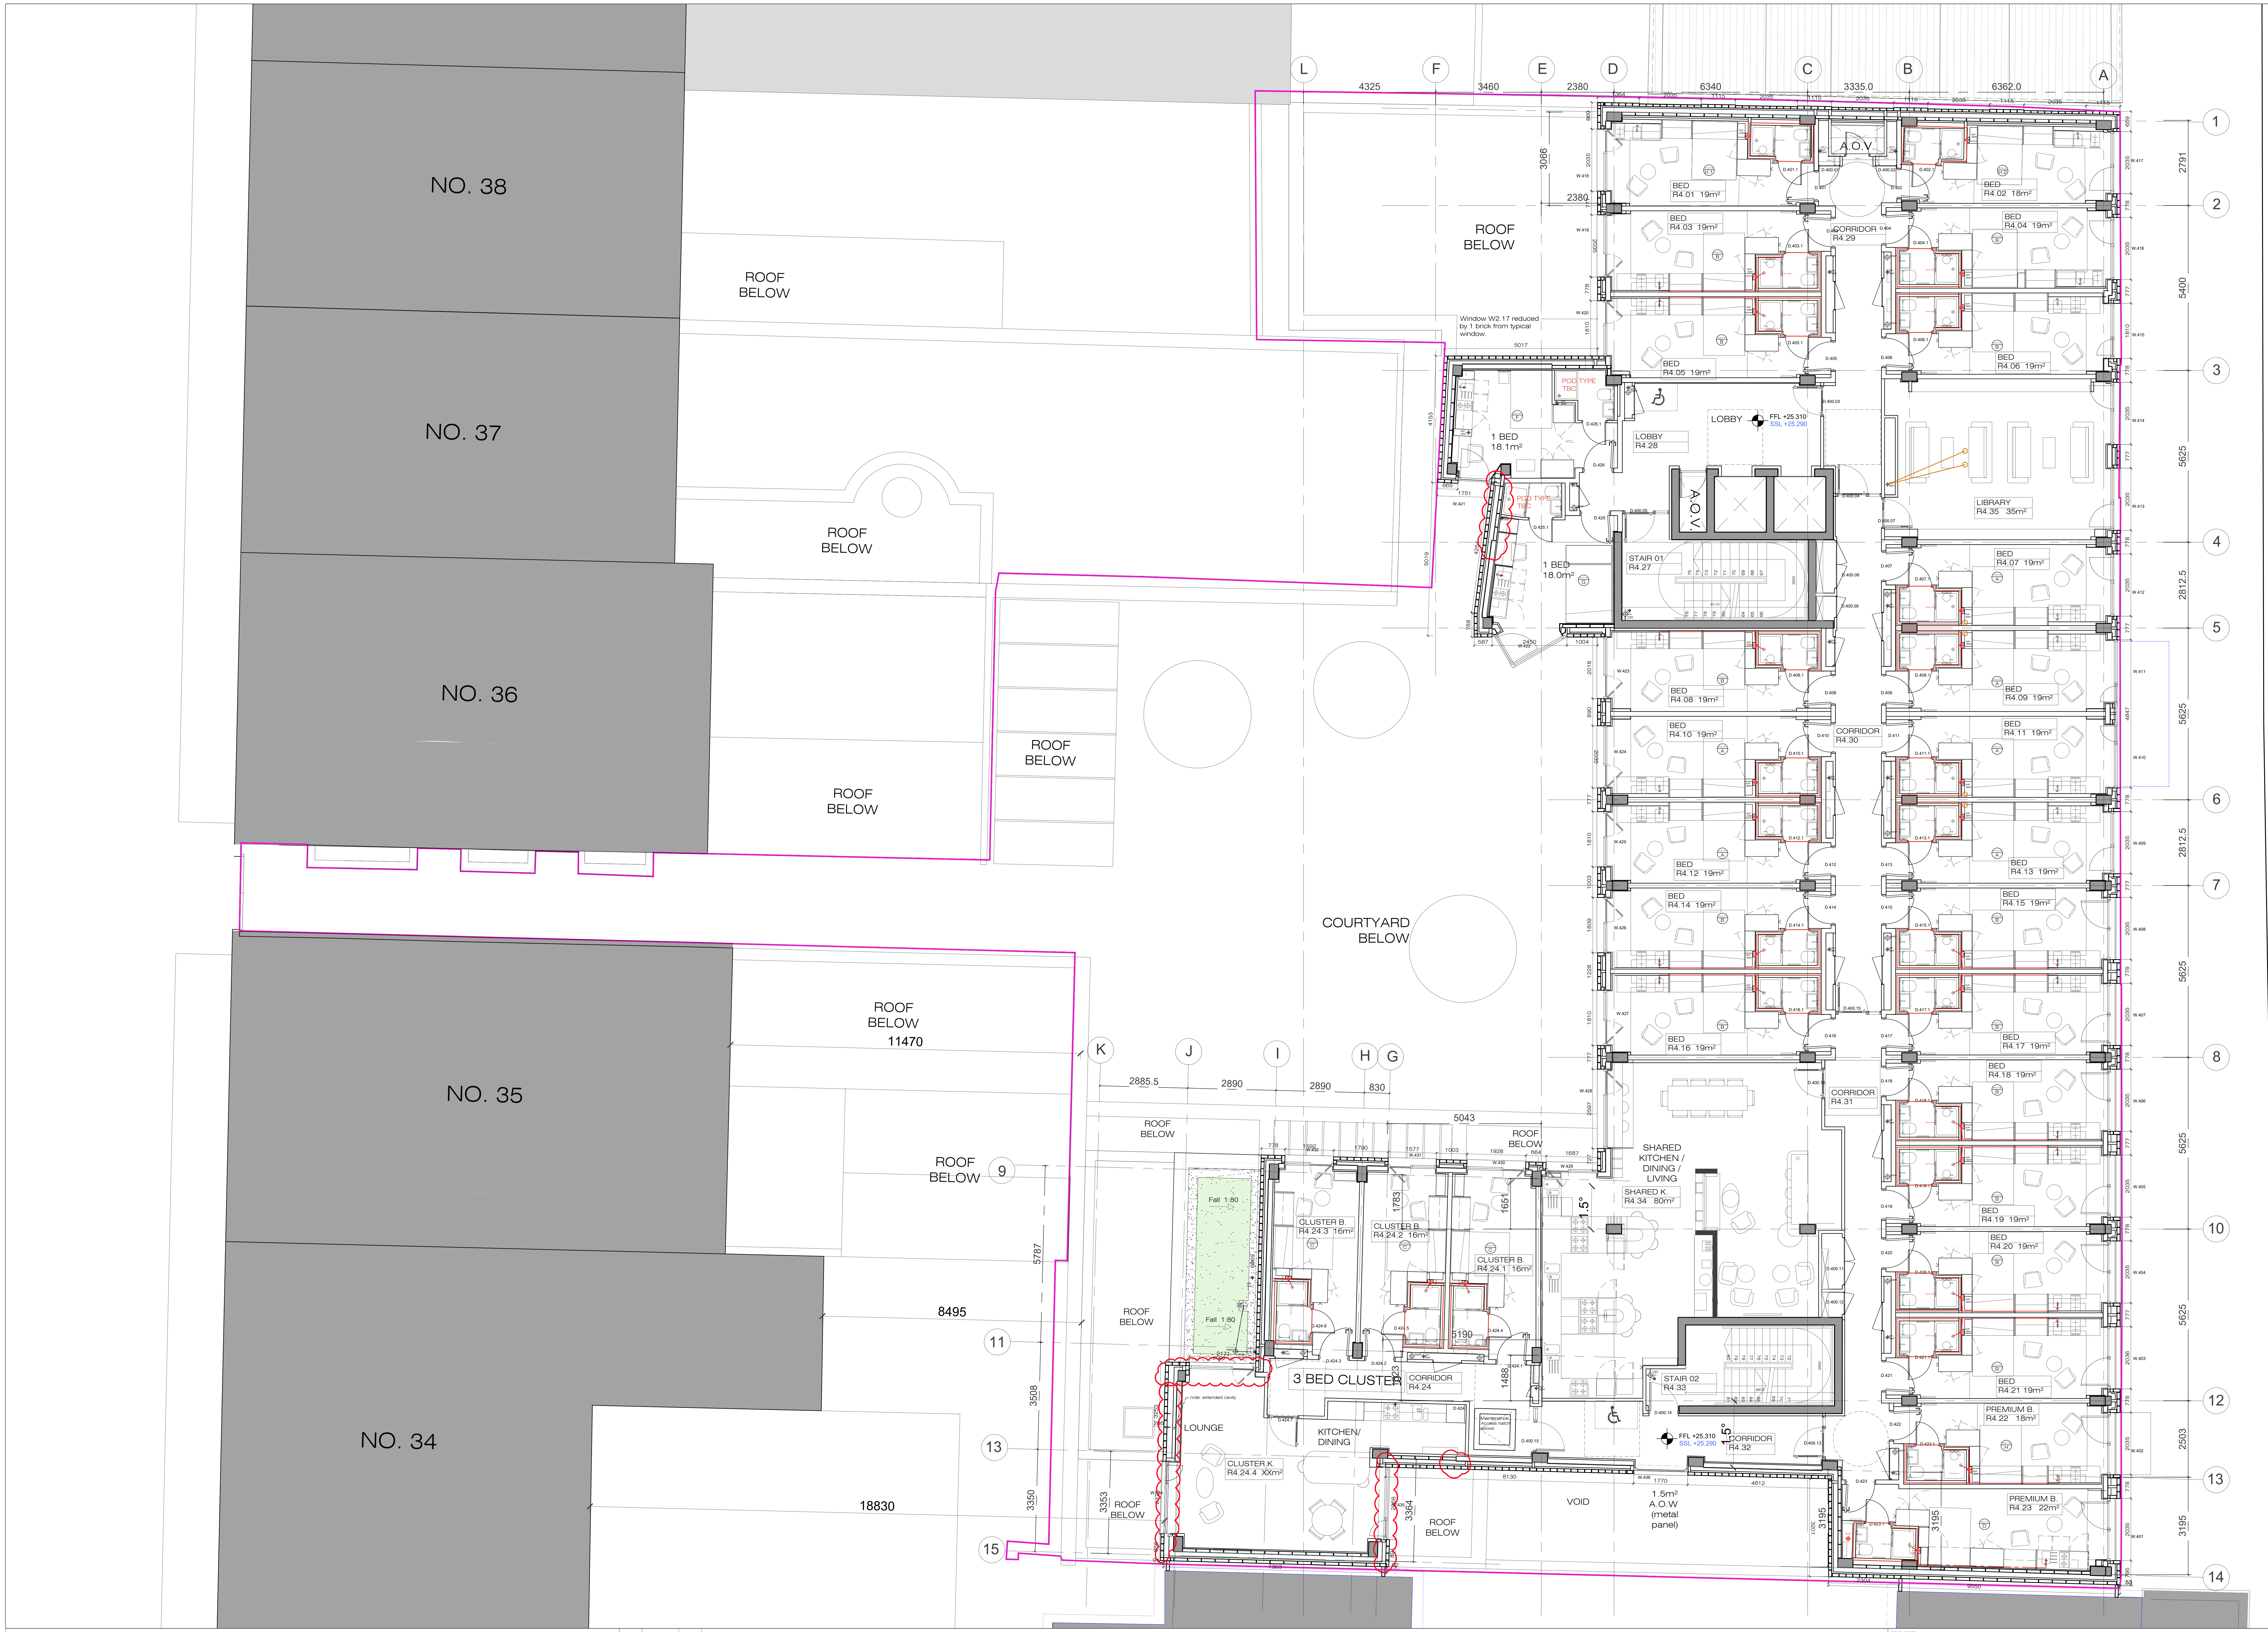
NO. 38
NO. 37
NO. 36
NO. 35
NO. 34
ROOF BELOW
COURTYARD BELOW
L
F
E
D
C
B
A
K
J
I
H
G
1
2
3
4
5
6
7
8
9
10
11
12
13
14
15
4325
3460
2380
6340
3335.0
6362.0
3066
2380
2791
5400
5625
2812.5
2503
3195
11470
8495
18830
5787
3508
3350
3353
3364
2885.5
2890
830
5043
5017
4153
5019
Window W2.17 reduced by 1 brick from typical window.
POD TYPE TBC
1 BED 18.1m²
1 BED 18.0m²
LOBBY R4.28
LOBBY
FFL +25.310
SSL +25.290
A.O.V.
STAIR 01 R4.27
CORRIDOR R4.29
CORRIDOR R4.30
CORRIDOR R4.31
CORRIDOR R4.32
CORRIDOR R4.24
LIBRARY R4.35 35m²
BED R4.01 19m²
BED R4.02 18m²
BED R4.03 19m²
BED R4.04 19m²
BED R4.05 19m²
BED R4.06 19m²
BED R4.07 19m²
BED R4.08 19m²
BED R4.09 19m²
BED R4.10 19m²
BED R4.11 19m²
BED R4.12 19m²
BED R4.13 19m²
BED R4.14 19m²
BED R4.15 19m²
BED R4.16 19m²
BED R4.17 19m²
BED R4.18 19m²
BED R4.19 19m²
BED R4.20 19m²
BED R4.21 19m²
PREMIUM B. R4.22 18m²
PREMIUM B. R4.23 22m²
SHARED KITCHEN / DINING / LIVING
SHARED K. R4.34 80m²
STAIR 02 R4.33
CLUSTER B. R4.24.3 16m²
CLUSTER B. R4.24.2 16m²
CLUSTER B. R4.24.1 16m²
CLUSTER K. R4.24.4 XXm²
3 BED CLUSTER
LOUNGE
KITCHEN/ DINING
Fall 1:80
note: extended cavity
Maintenance. Access hatch above.
VOID
1.5m² A.O.W (metal panel)
1.5°

NOTE:

POD OUTLINE AS PER
B-POD DRAWING.
BATHROOMS TO BE UPDATED

GENERAL NOTES

1. DO NOT SCALE FROM THIS DRAWING.
2. COPYRIGHT RESERVED TO DONNELLY TURPIN ARCHITECTS.
3. CONFIRM ALL DETAILS WITH JJC UNDERSLAB DRAWINGS AND AXIS ENG ABOVE SLAB SERVICES

REV.	DATE	NAME	NOTES
A	10.12.24	SC	REVISED NORTH CORRIDOR AOV. PART M TURNING AREA SHOWN IN CLUSTER
B	10.03.25	SC	ADDITION OF EXTERNAL BRICKWORK DIMENSIONS.
C	20.06.25	SC/AV	CHANGES TO INTERNAL DOORS AND PARTITIONS
D	22.07.25	MW	W.443 NARROWED TO SIMPLIFY SFS. BLOCKWORK ADDED. BRICK LINE CHANGED

PROJECT
38-42 HILL STREET and 36A NORTH GREAT GEORGE'S STREET
PROPOSED NEW CO-LIVING ACCOMMODATION

DONNELLY TURPIN ARCHITECTS
56 LOWER CAMDEN STREET, DUBLIN 2 TEL: (+353) 1 475 9065 E-MAIL : projects@donnellyturpin.com

STAGE	SCALE	DRAWING	
CONSTRUCTION	1:100 @ A1	GA-4TH FLOOR PLAN	
JOB NO.	DWG NO.	REV.	DATE
1843	C_03-005	E	JULY 2025