


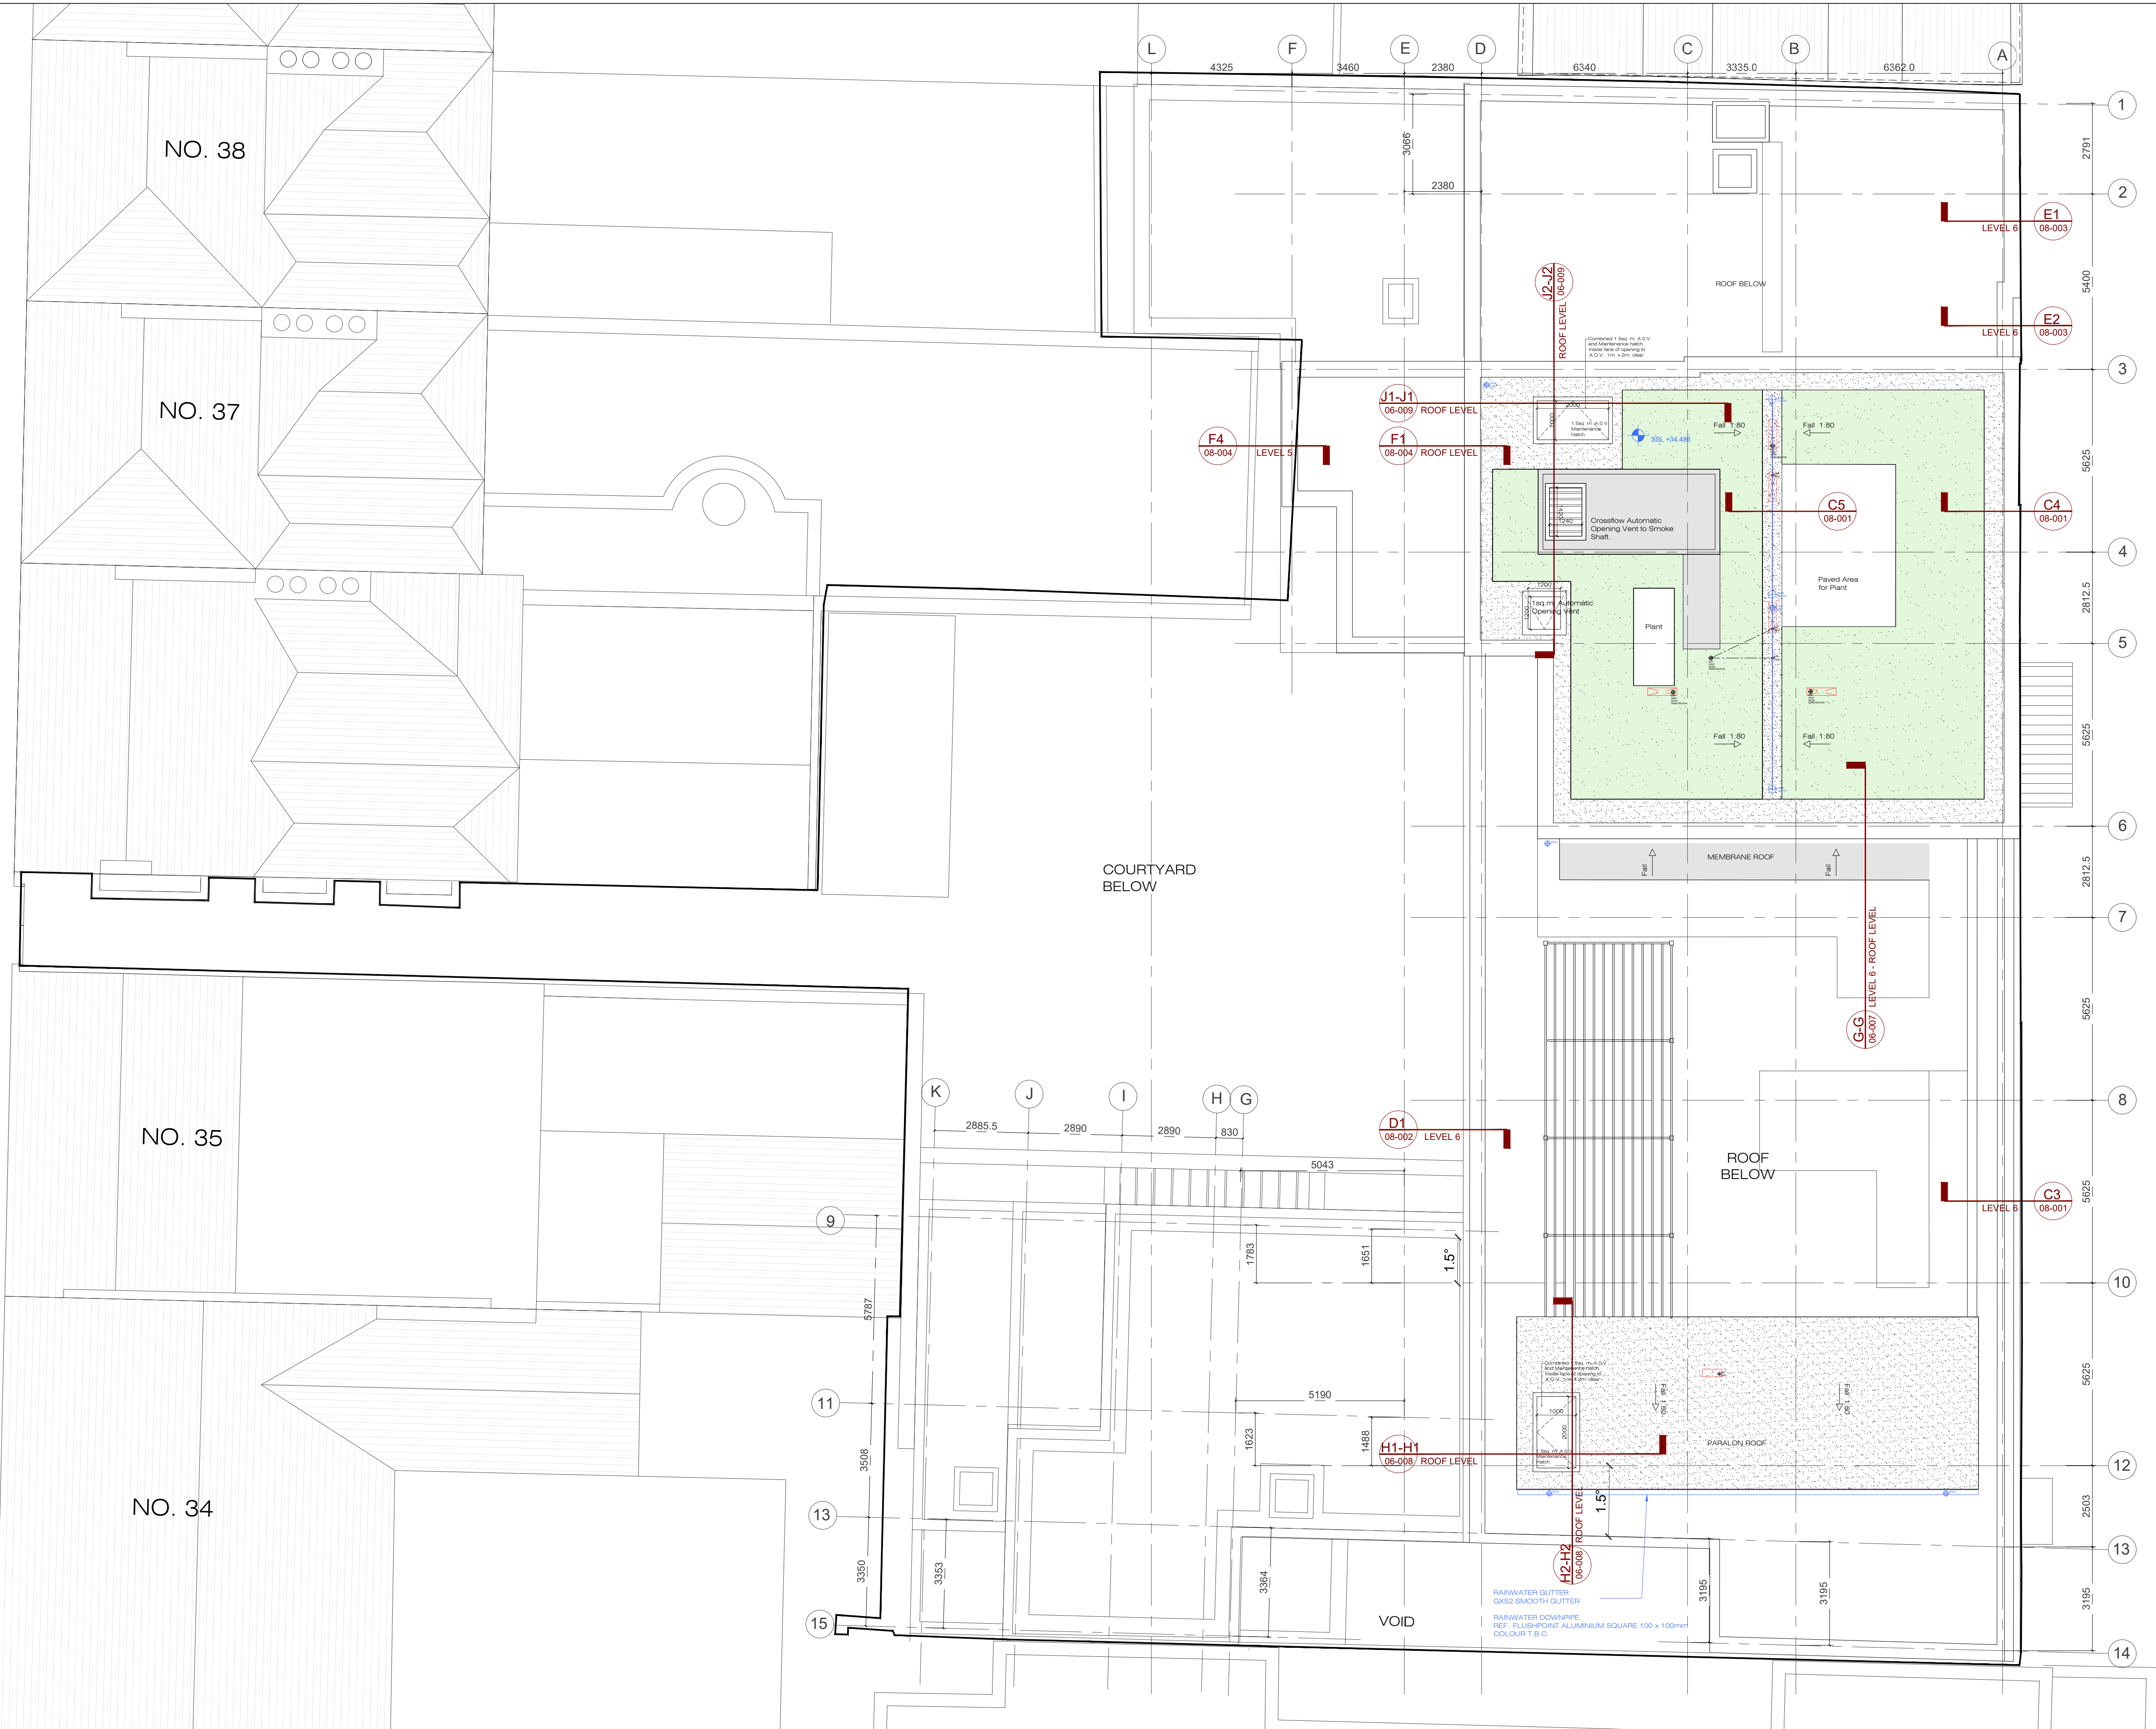

GENERAL NOTES

1. DO NOT SCALE FROM THIS DRAWING.
2. COPYRIGHT RESERVED TO DONNELLY TURPIN ARCHITECTS.
3. CONFIRM ALL DETAILS WITH JJC UNDERSLAB DRAWINGS AND AXIS
ENG ABOVE SLAB SERVICES

[illegible]

PROJECT			
38-42 HILL STREET and 36A NORTH GREAT GEORGE'S STREET			
PROPOSED NEW CO-LIVING ACCOMMODATION			
DONNELLY TURPIN ARCHITECTS			
56 LOWER CAMDEN STREET, DUBLIN 2			
TEL: (+353) 1 475 9005		E-MAIL: projects@donnellyturpin.com	
STAGE	SCALE	DRAWING	
CONSTRUCTION	1:100 @ A1	GA-ROOF PLAN	
JOB NO.	DWG NO.	REV.	DATE
1843	C_03-008		OCT 2024