


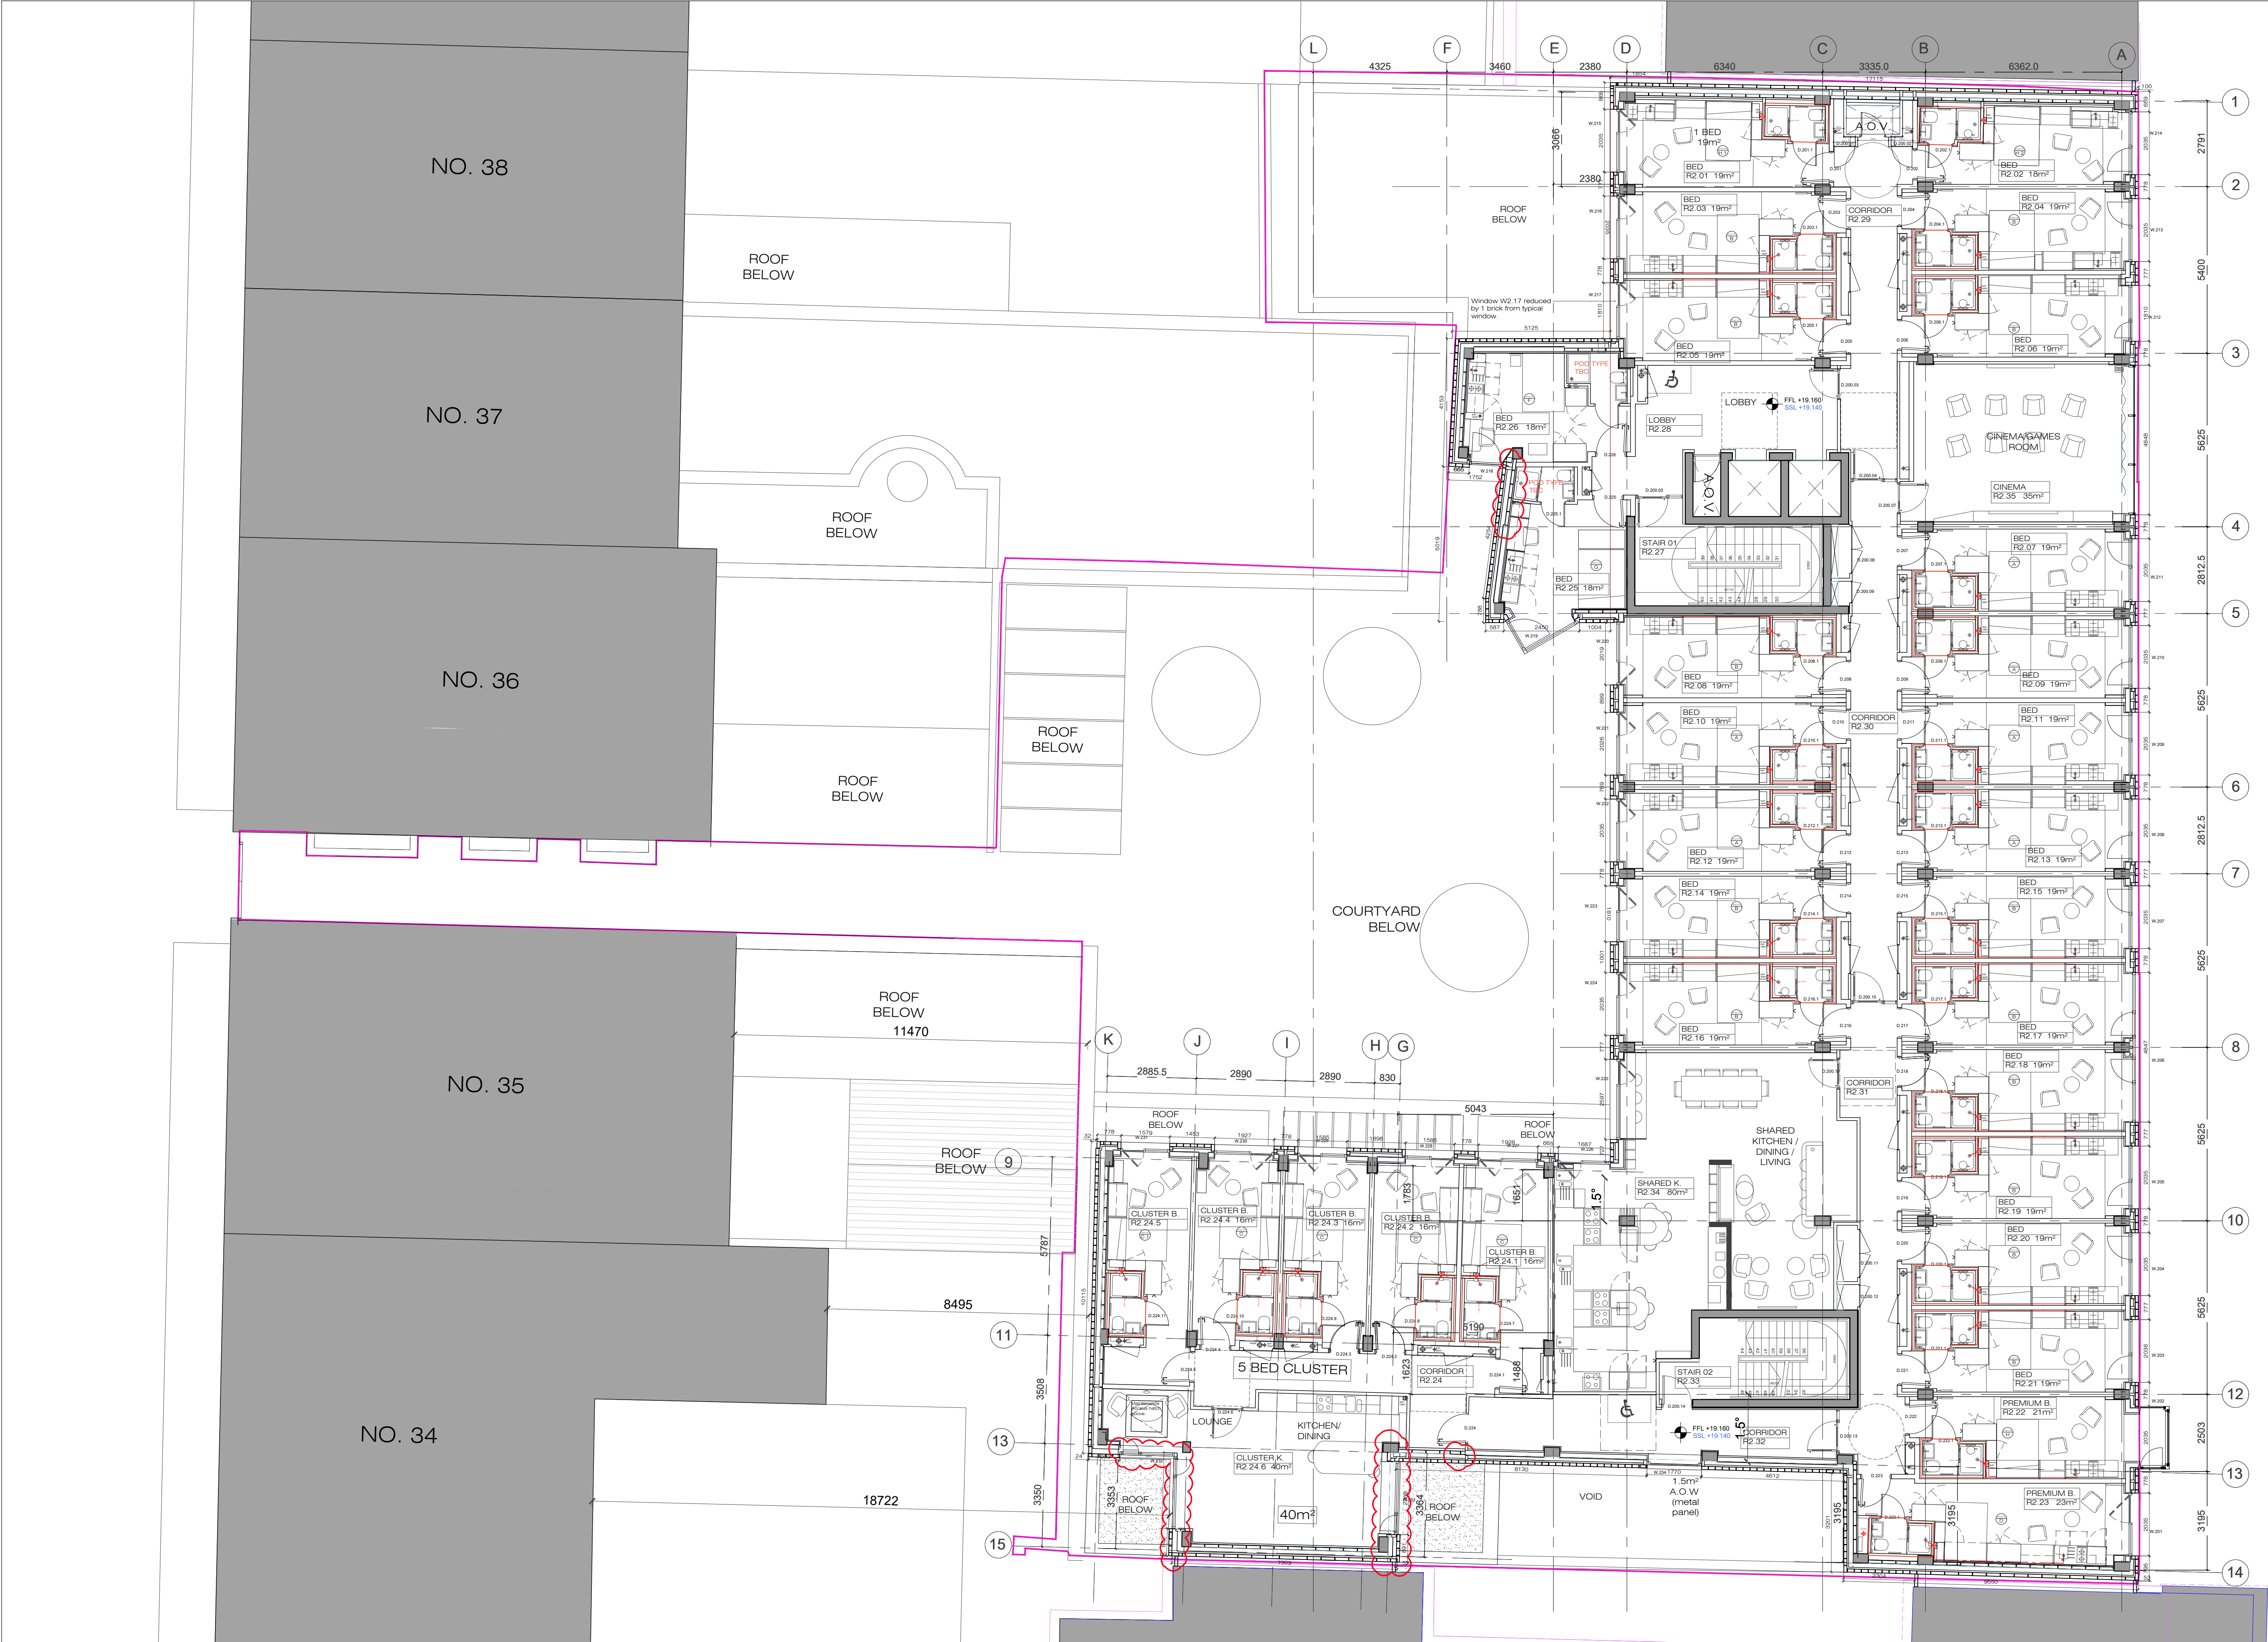

NOTE:

POD OUTLINE AS PER
B-POD DRAWING.
BATHROOMS TO BE UPDATED

GENERAL NOTES

- DO NOT SCALE FROM THIS DRAWING.
- COPYRIGHT RESERVED TO DONNELLY TURPIN ARCHITECTS.
- CONFIRM ALL DETAILS WITH JJC UNDERSLAB DRAWINGS AND AXIS ENG ABOVE SLAB SERVICES

REV.	DATE	NAME	NOTES
A	10.12.24	SC/MW	REVISED NORTH CORRIDOR A.O.V. COLUMN J-8 HAS BEEN MOVED 225 MM TOWARDS GRIDLINE 1. PART M TURNING AREA SHOWN IN CLUSTER
B	10.03.25	SC	ADDITION OF EXTERNAL BRICKWORK DIMENSIONS.
C	20.06.25	SC/JV	CHANGES TO INTERNAL DOORS AND PARTITIONS
D	22.07.25	SC	BLOCKWORK ADDED. BRICK LINE CHANGED

PROJECT
38-42 HILL STREET and 36A NORTH GREAT GEORGE'S STREET
PROPOSED NEW CO-LIVING ACCOMMODATION

DONNELLY TURPIN ARCHITECTS
56 LOWER CAMDEN STREET, DUBLIN 2 TEL: (+353) 1 475 9065 E-MAIL: projects@donnellyturpin.com

STAGE	SCALE	DRAWING	GENERAL ARRANGEMENT:
CONSTRUCTION	1:100 @ A1		SECOND FLOOR PLAN
JOB NO. 1843	DWG NO. C_03-003	REV. D	DATE JULY 2025