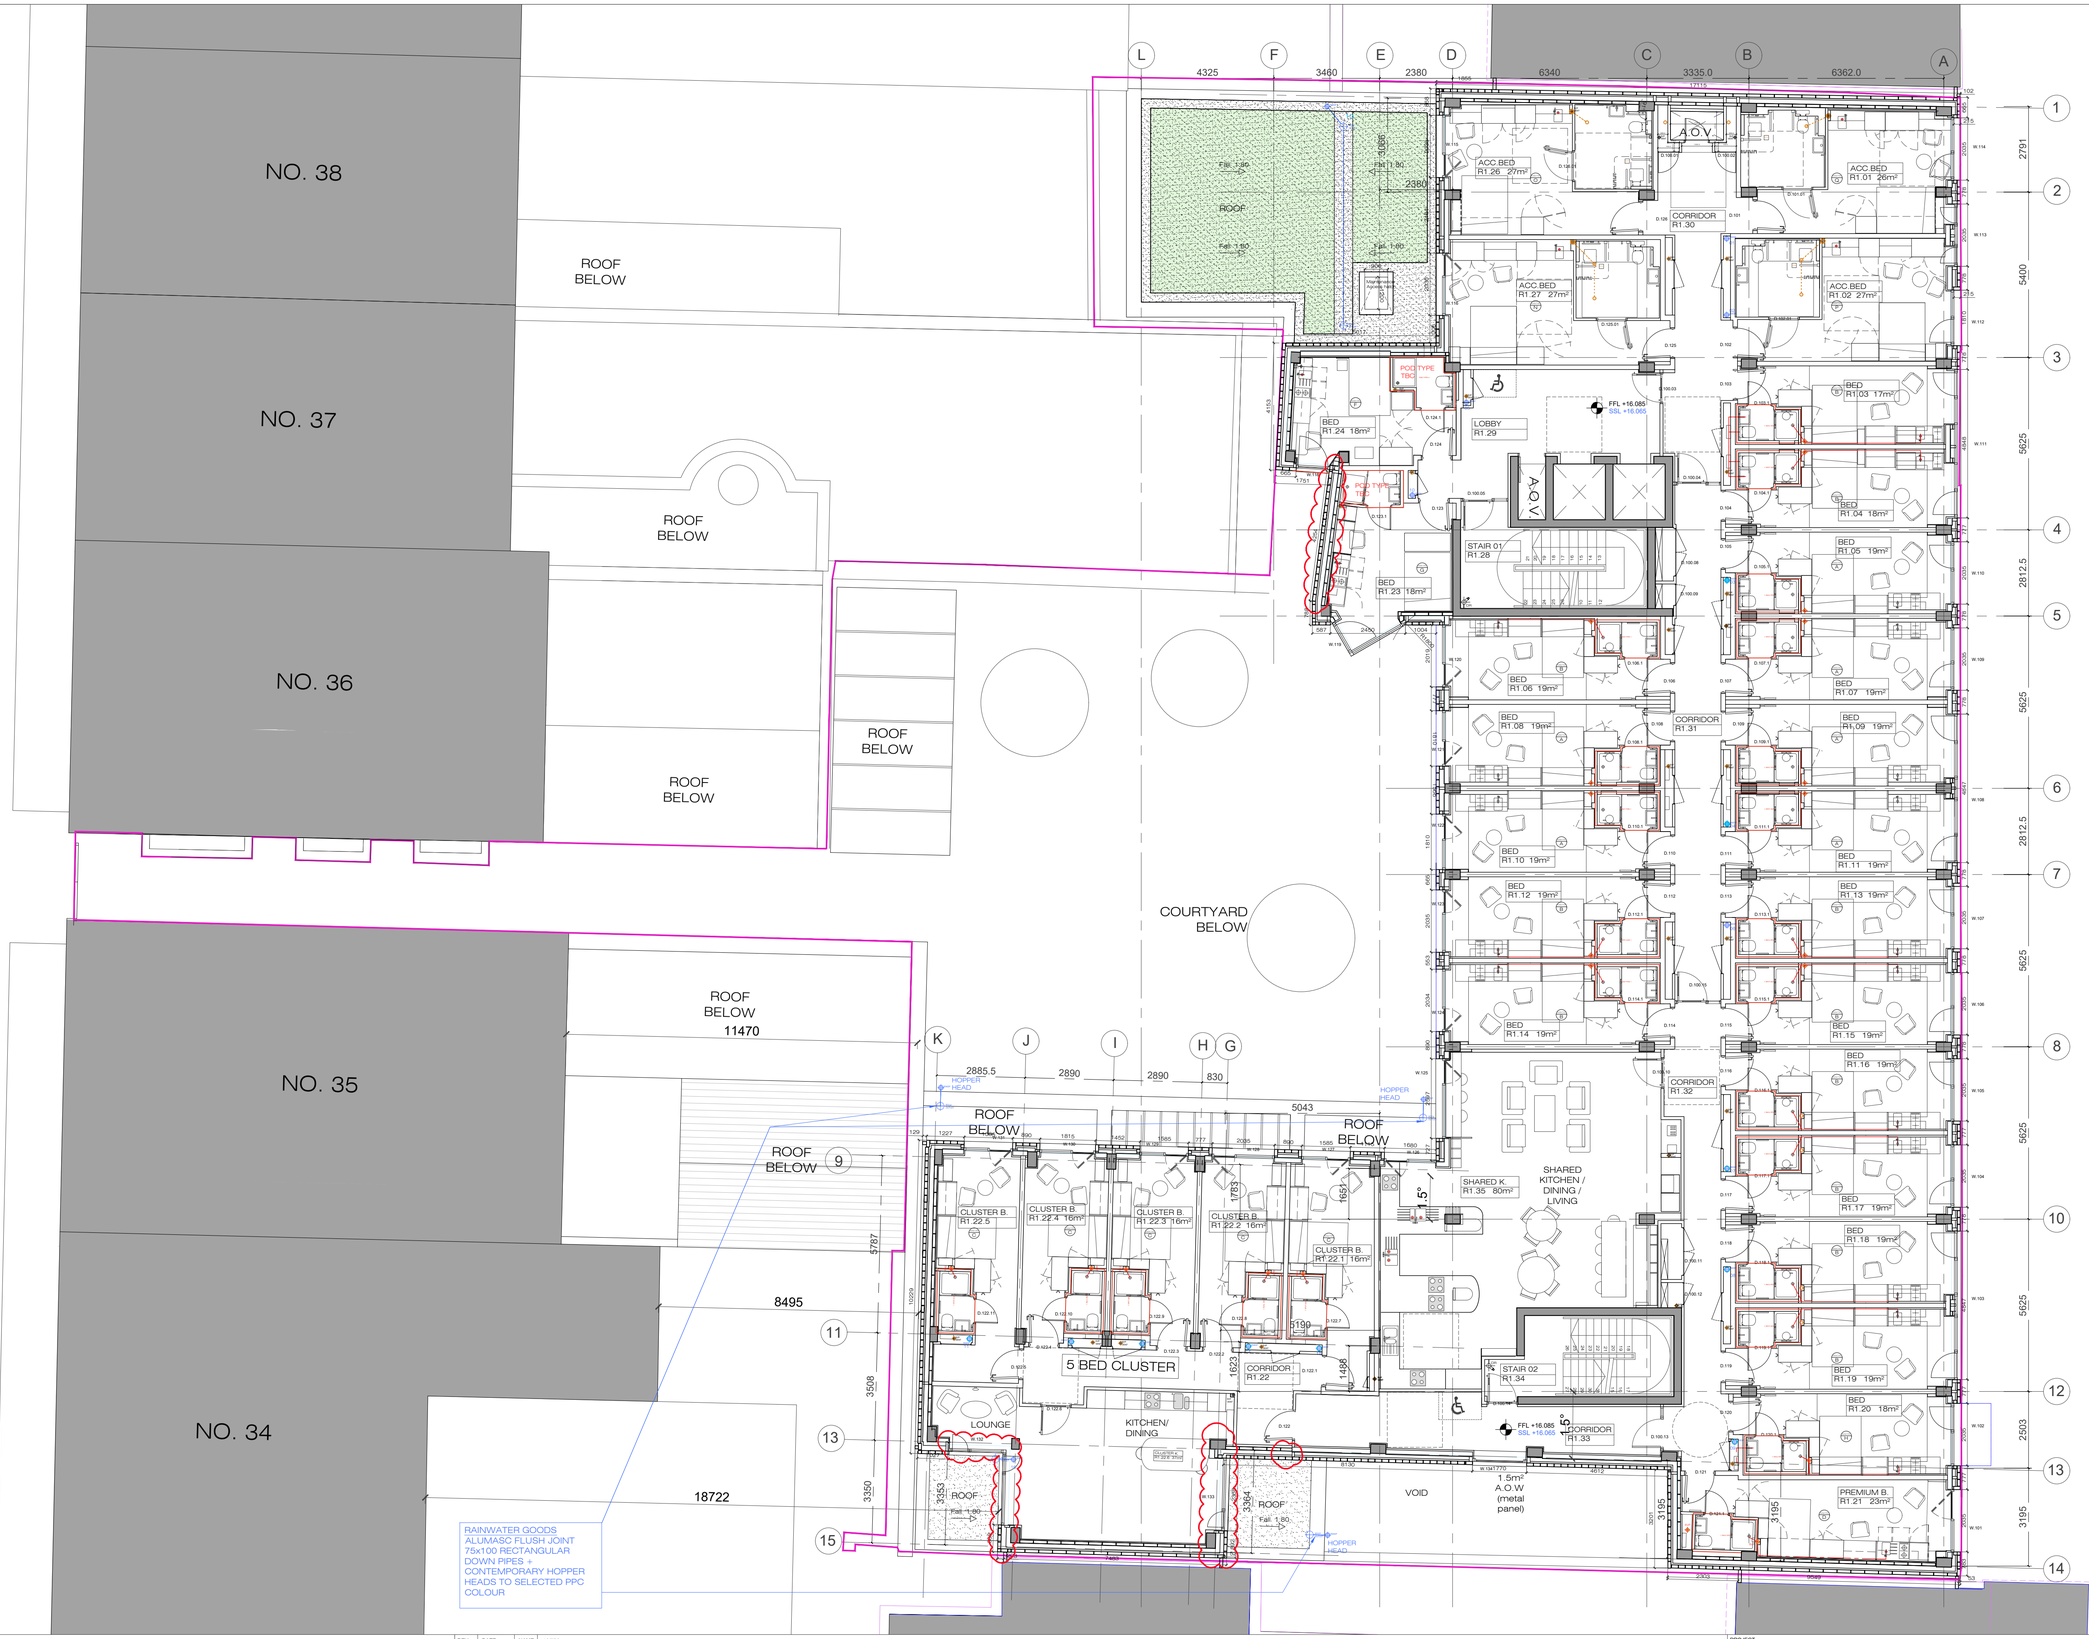


GENERAL NOTES

1. DO NOT SCALE FROM THIS DRAWING.
2. COPYRIGHT RESERVED TO DONNELLY TURPIN ARCHITECTS.
3. CONFIRM ALL DETAILS WITH JJC UNDERSLAB DRAWINGS AND AXIS ENG ABOVE SLAB SERVICES

REV.	DATE	NAME	NOTES
A	10.12.24	SC/MW	REVISED NORTH CORRIDOR AOV. COLUMN J-9 HAS BEEN MOVED 225 MM TOWARDS GRIDLINE I. PART M TURNING AREA SHOWN IN CLUSTER
B	10.03.25	SC	ADDITION OF EXTERNAL BRICKWORK DIMENSIONS.
C	20.06.25	SC/AV	CHANGES TO INTERNAL DOORS AND PARTITIONS
D	22.07.25	SC	BLOCKWORK ADDED. BRICK LINE CHANGED

PROJECT
38-42 HILL STREET and 36A NORTH GREAT GEORGE'S STREET
PROPOSED NEW CO-LIVING ACCOMMODATION

DONNELLY TURPIN ARCHITECTS
56 LOWER CAMDEN STREET, DUBLIN 2 TEL: (+353) 1 475 9065 E-MAIL : projects@donnellyturpin.com

STAGE	SCALE	DRAWING
CONSTRUCTION	1:100 @ A1	GA-1ST FLOOR PLAN

JOB NO.	DWG NO.	REV.	DATE
1843	C_03-002	D	JULY 2025