


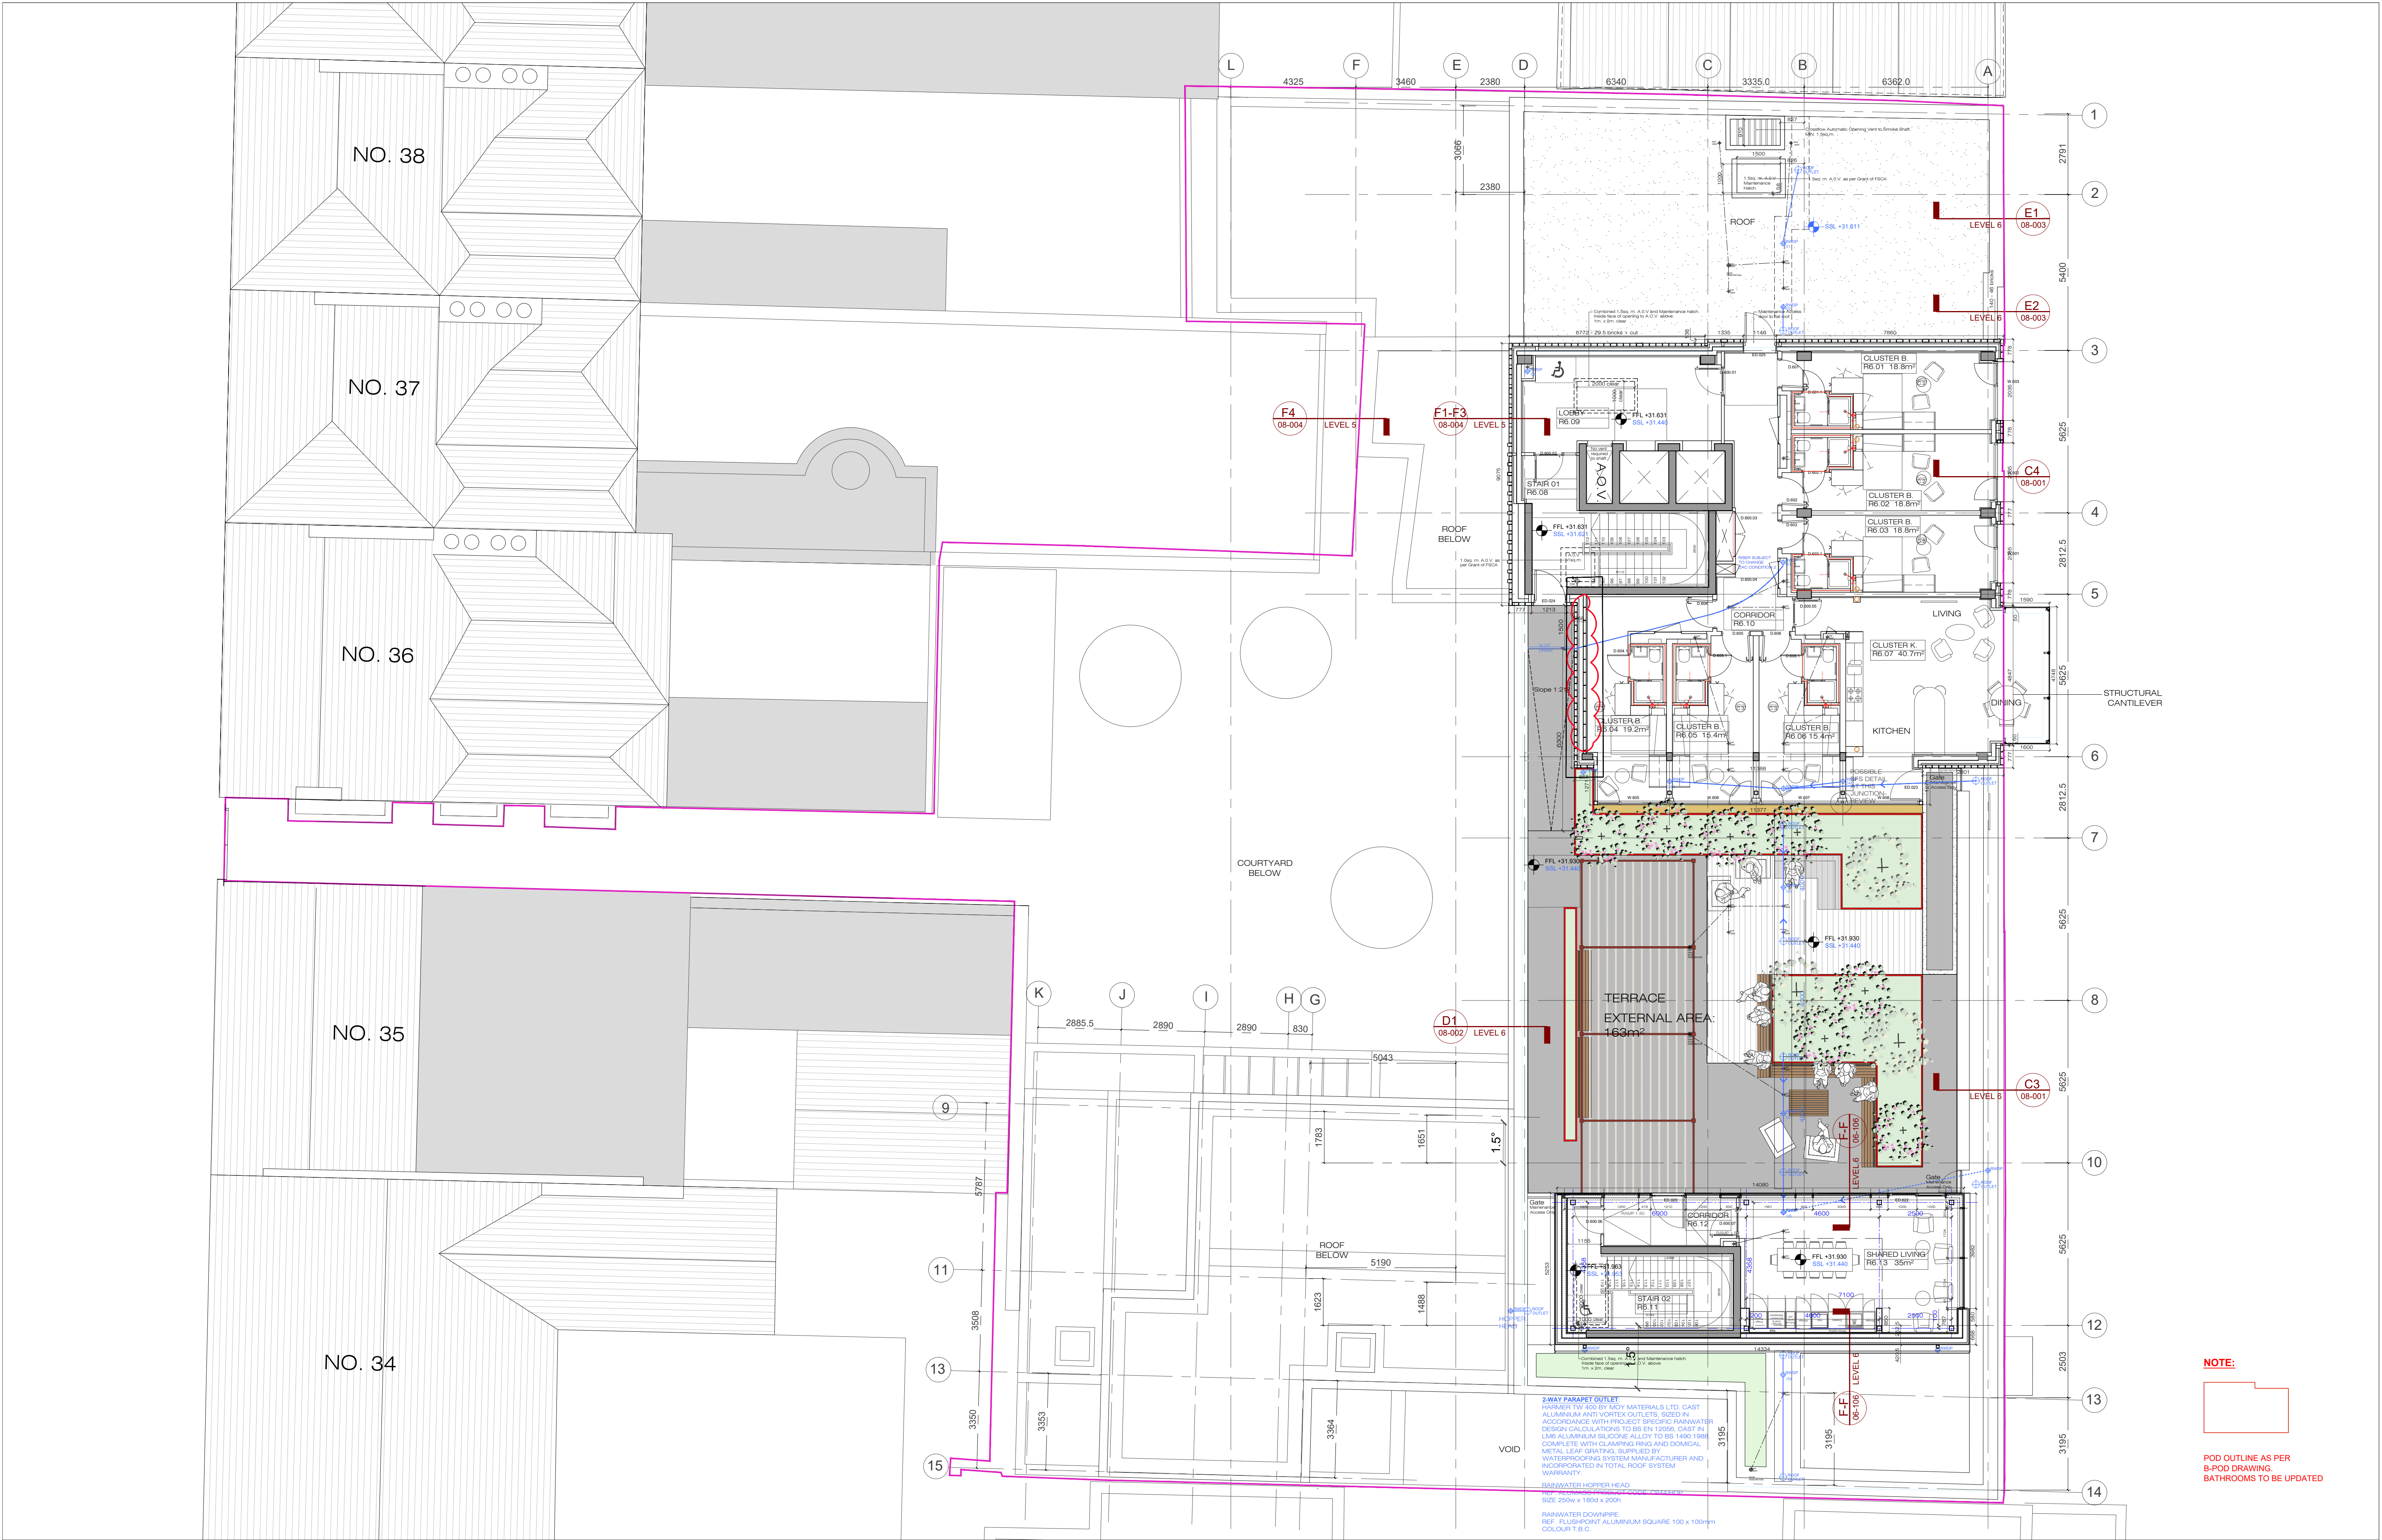

GENERAL NOTES 1. DO NOT SCALE FROM THIS DRAWING. 2. COPYRIGHT RESERVED TO DONNELLY TURPIN ARCHITECTS. 3. CONFIRM ALL DETAILS WITH JJC UNDERSLAB DRAWINGS AND AXIS ENG ABOVE SLAB SERVICES				<table><tr><th>REV.</th><th>DATE</th><th>NAME</th><th>NOTES</th></tr><tr><td>A</td><td>10.12.24</td><td>SC</td><td>REVISED CLUSTER CORRIDOR, RISERS AND TURNING CIRCLES. REVISED LANDINGS TO STAIR 2</td></tr><tr><td>B</td><td>06.03.25</td><td>SC</td><td>SSL LEVELS UPDATED IN CORES</td></tr><tr><td>C</td><td>10.03.25</td><td>SC</td><td>ADDITION OF EXTERNAL BRICKWORK DIMENSIONS</td></tr><tr><td>D</td><td>12.06.25</td><td>SC/AV</td><td>CHANGES TO INTERNAL DOORS AND PARTITIONS</td></tr><tr><td>E</td><td>22.07.25</td><td>SC</td><td>ADDITIONAL BLOCKWORK AREA</td></tr><tr><td> </td><td> </td><td> </td><td> </td></tr><tr><td> </td><td> </td><td> </td><td> </td></tr><tr><td> </td><td> </td><td> </td><td> </td></tr><tr><td> </td><td> </td><td> </td><td> </td></tr><tr><td> </td><td> </td><td> </td><td> </td></tr></table>				REV.	DATE	NAME	NOTES	A	10.12.24	SC	REVISED CLUSTER CORRIDOR, RISERS AND TURNING CIRCLES. REVISED LANDINGS TO STAIR 2	B	06.03.25	SC	SSL LEVELS UPDATED IN CORES	C	10.03.25	SC	ADDITION OF EXTERNAL BRICKWORK DIMENSIONS	D	12.06.25	SC/AV	CHANGES TO INTERNAL DOORS AND PARTITIONS	E	22.07.25	SC	ADDITIONAL BLOCKWORK AREA																					<table><tr><td colspan="4">PROJECT</td></tr><tr><td colspan="4">38-42 HILL STREET and 36A NORTH GREAT GEORGE'S STREET</td></tr><tr><td colspan="4">PROPOSED NEW CO-LIVING ACCOMMODATION</td></tr><tr><td colspan="4">DONNELLY TURPIN ARCHITECTS</td></tr><tr><td colspan="4">56 LOWER CAMDEN STREET, DUBLIN 2 TEL: (+353) 1 475 9065 E-MAIL: projects@donnellyturpin.com</td></tr><tr><td colspan="2">STAGE</td><td>SCALE</td><td>DRAWING</td></tr><tr><td colspan="2">CONSTRUCTION</td><td>1:100 @ A1</td><td>GA-6TH FLOOR PLAN</td></tr><tr><td colspan="2">JOB NO.</td><td>DWG NO.</td><td>REV.</td></tr><tr><td colspan="2">1843</td><td>C_03-007</td><td>E</td></tr><tr><td colspan="2"></td><td></td><td>DATE</td></tr><tr><td colspan="2"></td><td></td><td>JULY 2025</td></tr></table>				PROJECT				38-42 HILL STREET and 36A NORTH GREAT GEORGE'S STREET				PROPOSED NEW CO-LIVING ACCOMMODATION				DONNELLY TURPIN ARCHITECTS				56 LOWER CAMDEN STREET, DUBLIN 2 TEL: (+353) 1 475 9065 E-MAIL: projects@donnellyturpin.com				STAGE		SCALE	DRAWING	CONSTRUCTION		1:100 @ A1	GA-6TH FLOOR PLAN	JOB NO.		DWG NO.	REV.	1843		C_03-007	E				DATE				JULY 2025
REV.	DATE	NAME	NOTES	
A	10.12.24	SC	REVISED CLUSTER CORRIDOR, RISERS AND TURNING CIRCLES. REVISED LANDINGS TO STAIR 2	
B	06.03.25	SC	SSL LEVELS UPDATED IN CORES	
C	10.03.25	SC	ADDITION OF EXTERNAL BRICKWORK DIMENSIONS	
D	12.06.25	SC/AV	CHANGES TO INTERNAL DOORS AND PARTITIONS	
E	22.07.25	SC	ADDITIONAL BLOCKWORK AREA	
PROJECT	
38-42 HILL STREET and 36A NORTH GREAT GEORGE'S STREET	
PROPOSED NEW CO-LIVING ACCOMMODATION	
DONNELLY TURPIN ARCHITECTS	
56 LOWER CAMDEN STREET, DUBLIN 2 TEL: (+353) 1 475 9065 E-MAIL: projects@donnellyturpin.com	
STAGE		SCALE	DRAWING	
CONSTRUCTION		1:100 @ A1	GA-6TH FLOOR PLAN	
JOB NO.		DWG NO.	REV.	
1843		C_03-007	E	
			DATE	
			JULY 2025	