


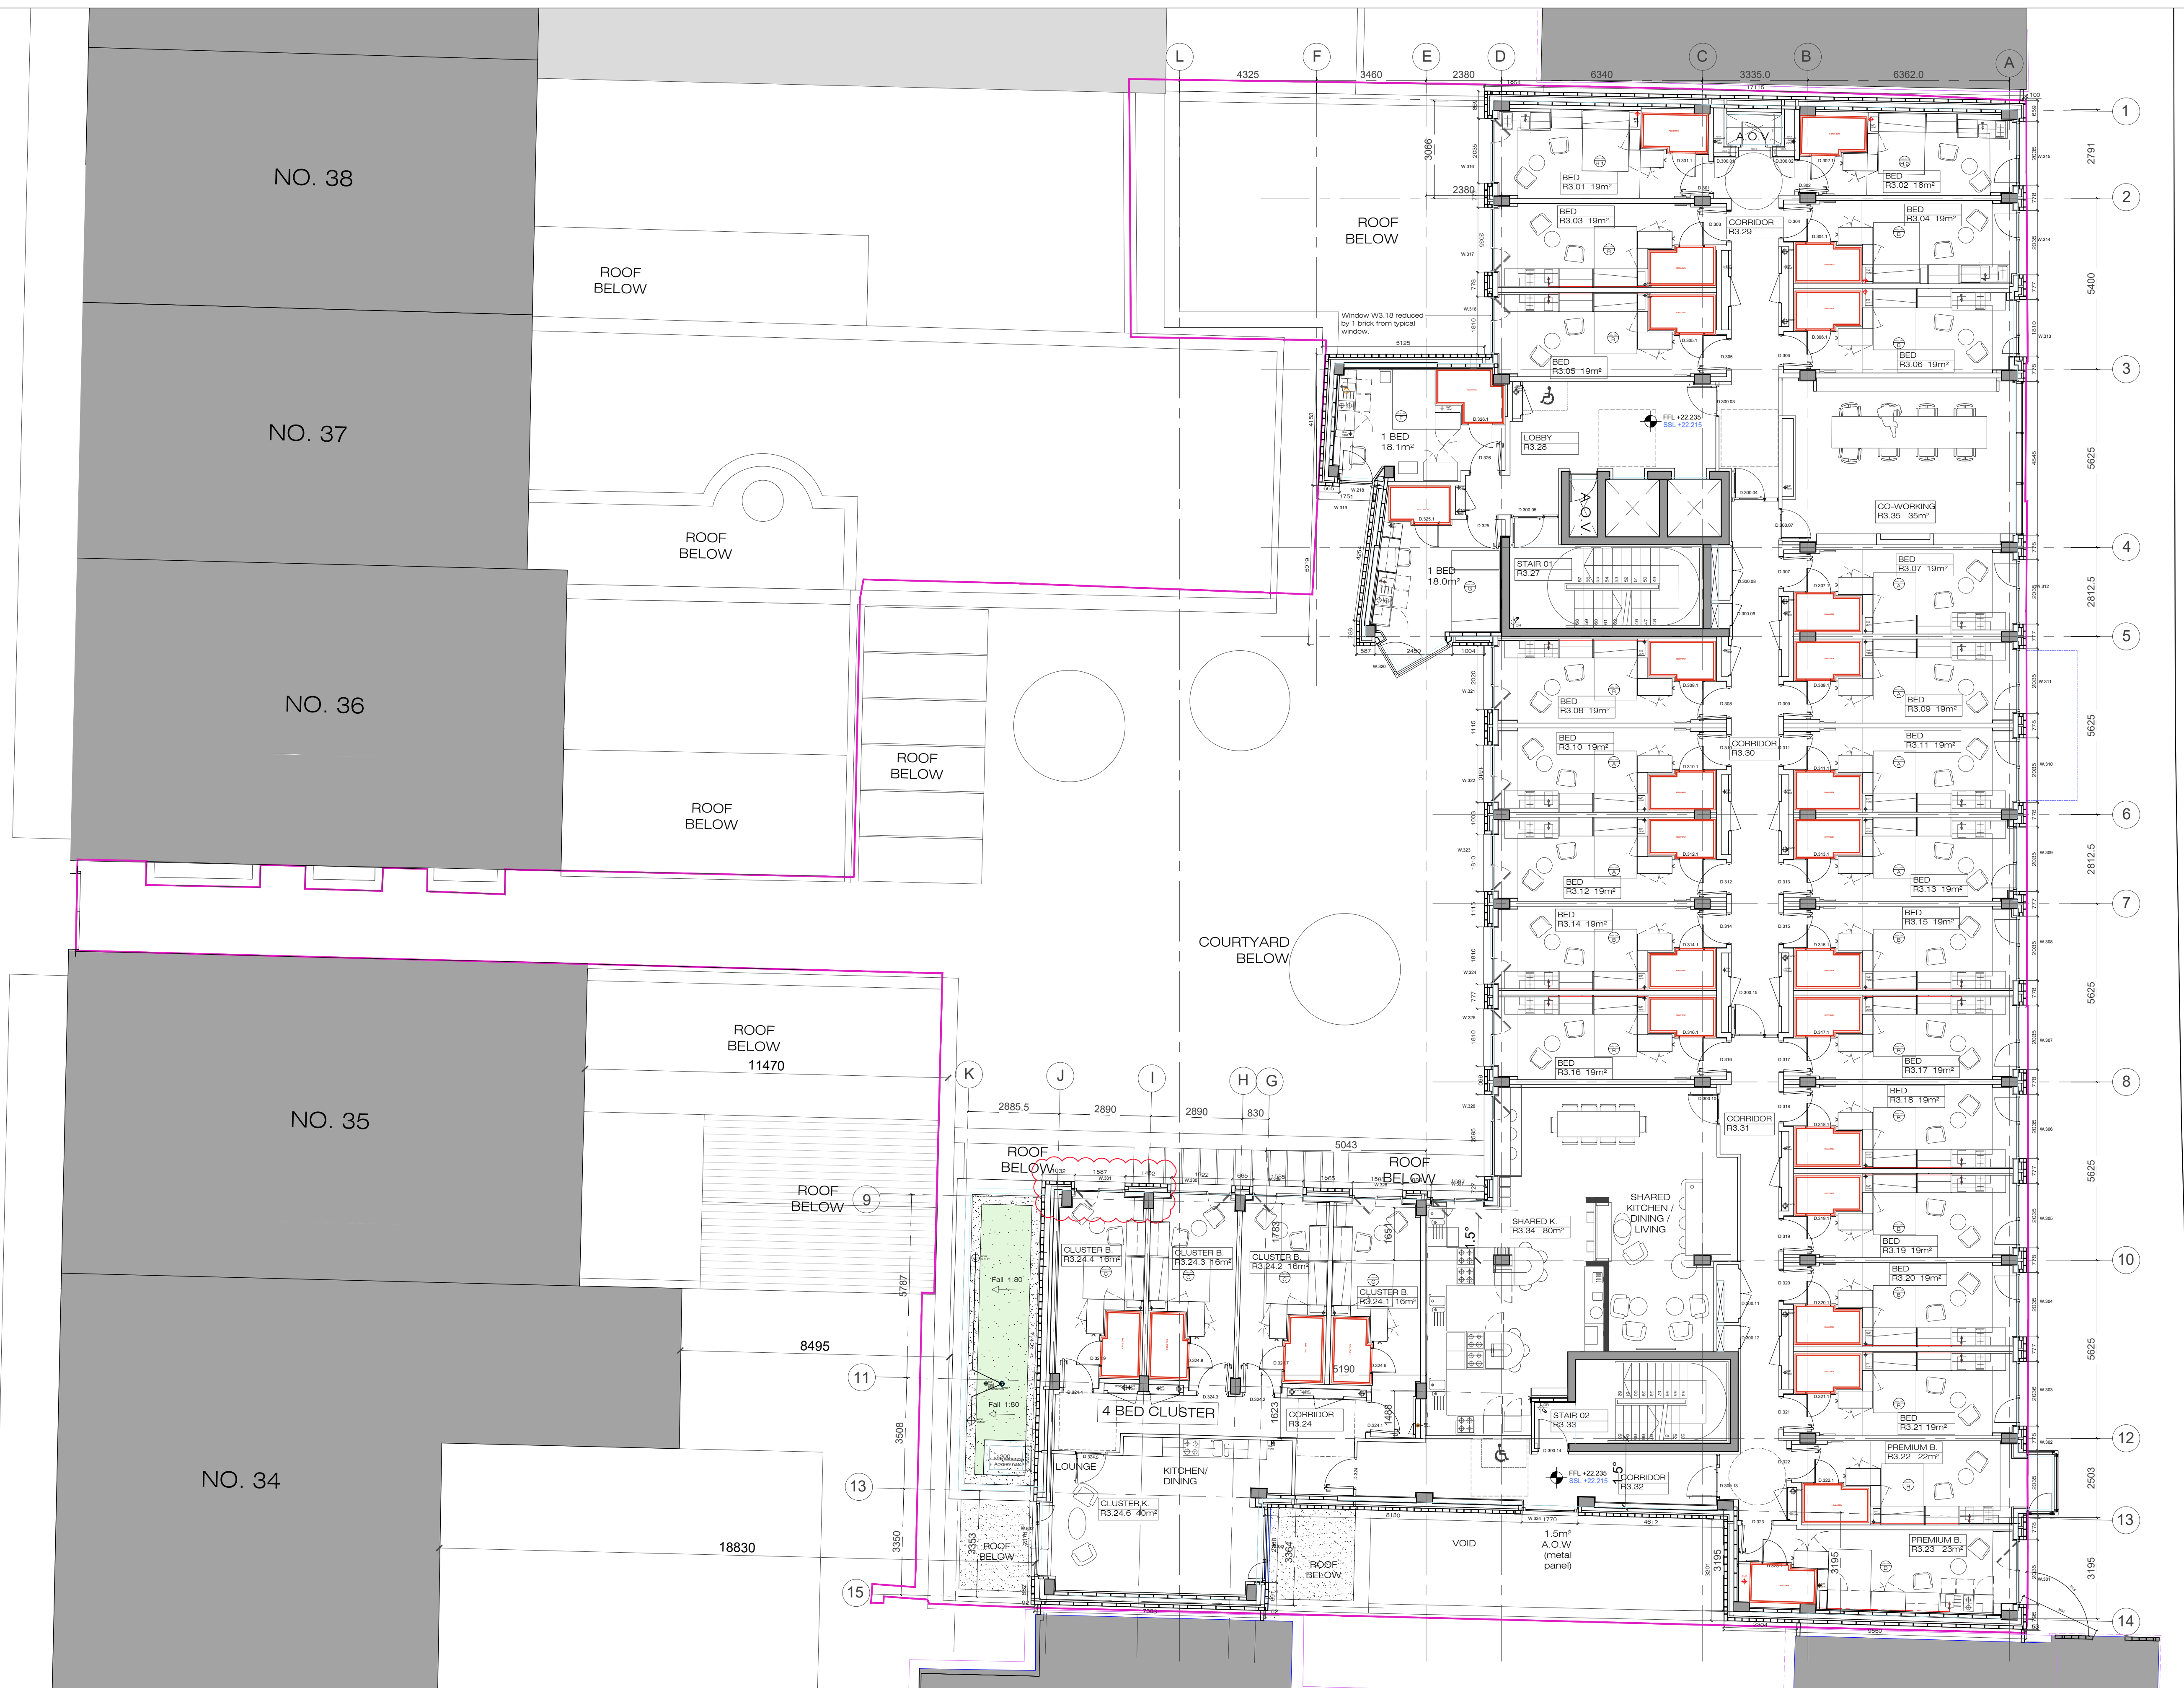

PROJECT	38-42 HILL STREET and 36A NORTH GREAT GEORGE'S STREET PROPOSED NEW CO-LIVING ACCOMMODATION		
DONNELLY TURPIN ARCHITECTS 56 LOWER CAMDEN STREET, DUBLIN 2 TEL: (+353) 1 475 9665 E-MAIL: projects@donnellyturpin.com			
STAGE	SCALE	DRAWING	
CONSTRUCTION	1:100 @ A1	GA-3RD FLOOR PLAN	
JOB NO.	DWG. NO.	REV.	DATE
1843	C_03-004	E	SEPT 2025